



LEGEND

SAFETY TRAINING & FIRST AID STATION	
REST AREA	
WATER STATION	
TOILET	
STORE AREA	
SPEED HUMP	
STOCK PILE	
WORKERS PICKUP & DROP OFF POINTS	
TRAFFICE SIGNS BOARD	
SITE OFFICES	
Container	
FIRE FIGHTING POINT	
LOGISTIC ROAD	
ENTRANCE GATE	
ROUND ABOUT	
THIS LOGISTIC PLAN WILL CHANGE DURING THE COURSE OF CONSTRUCTION.	

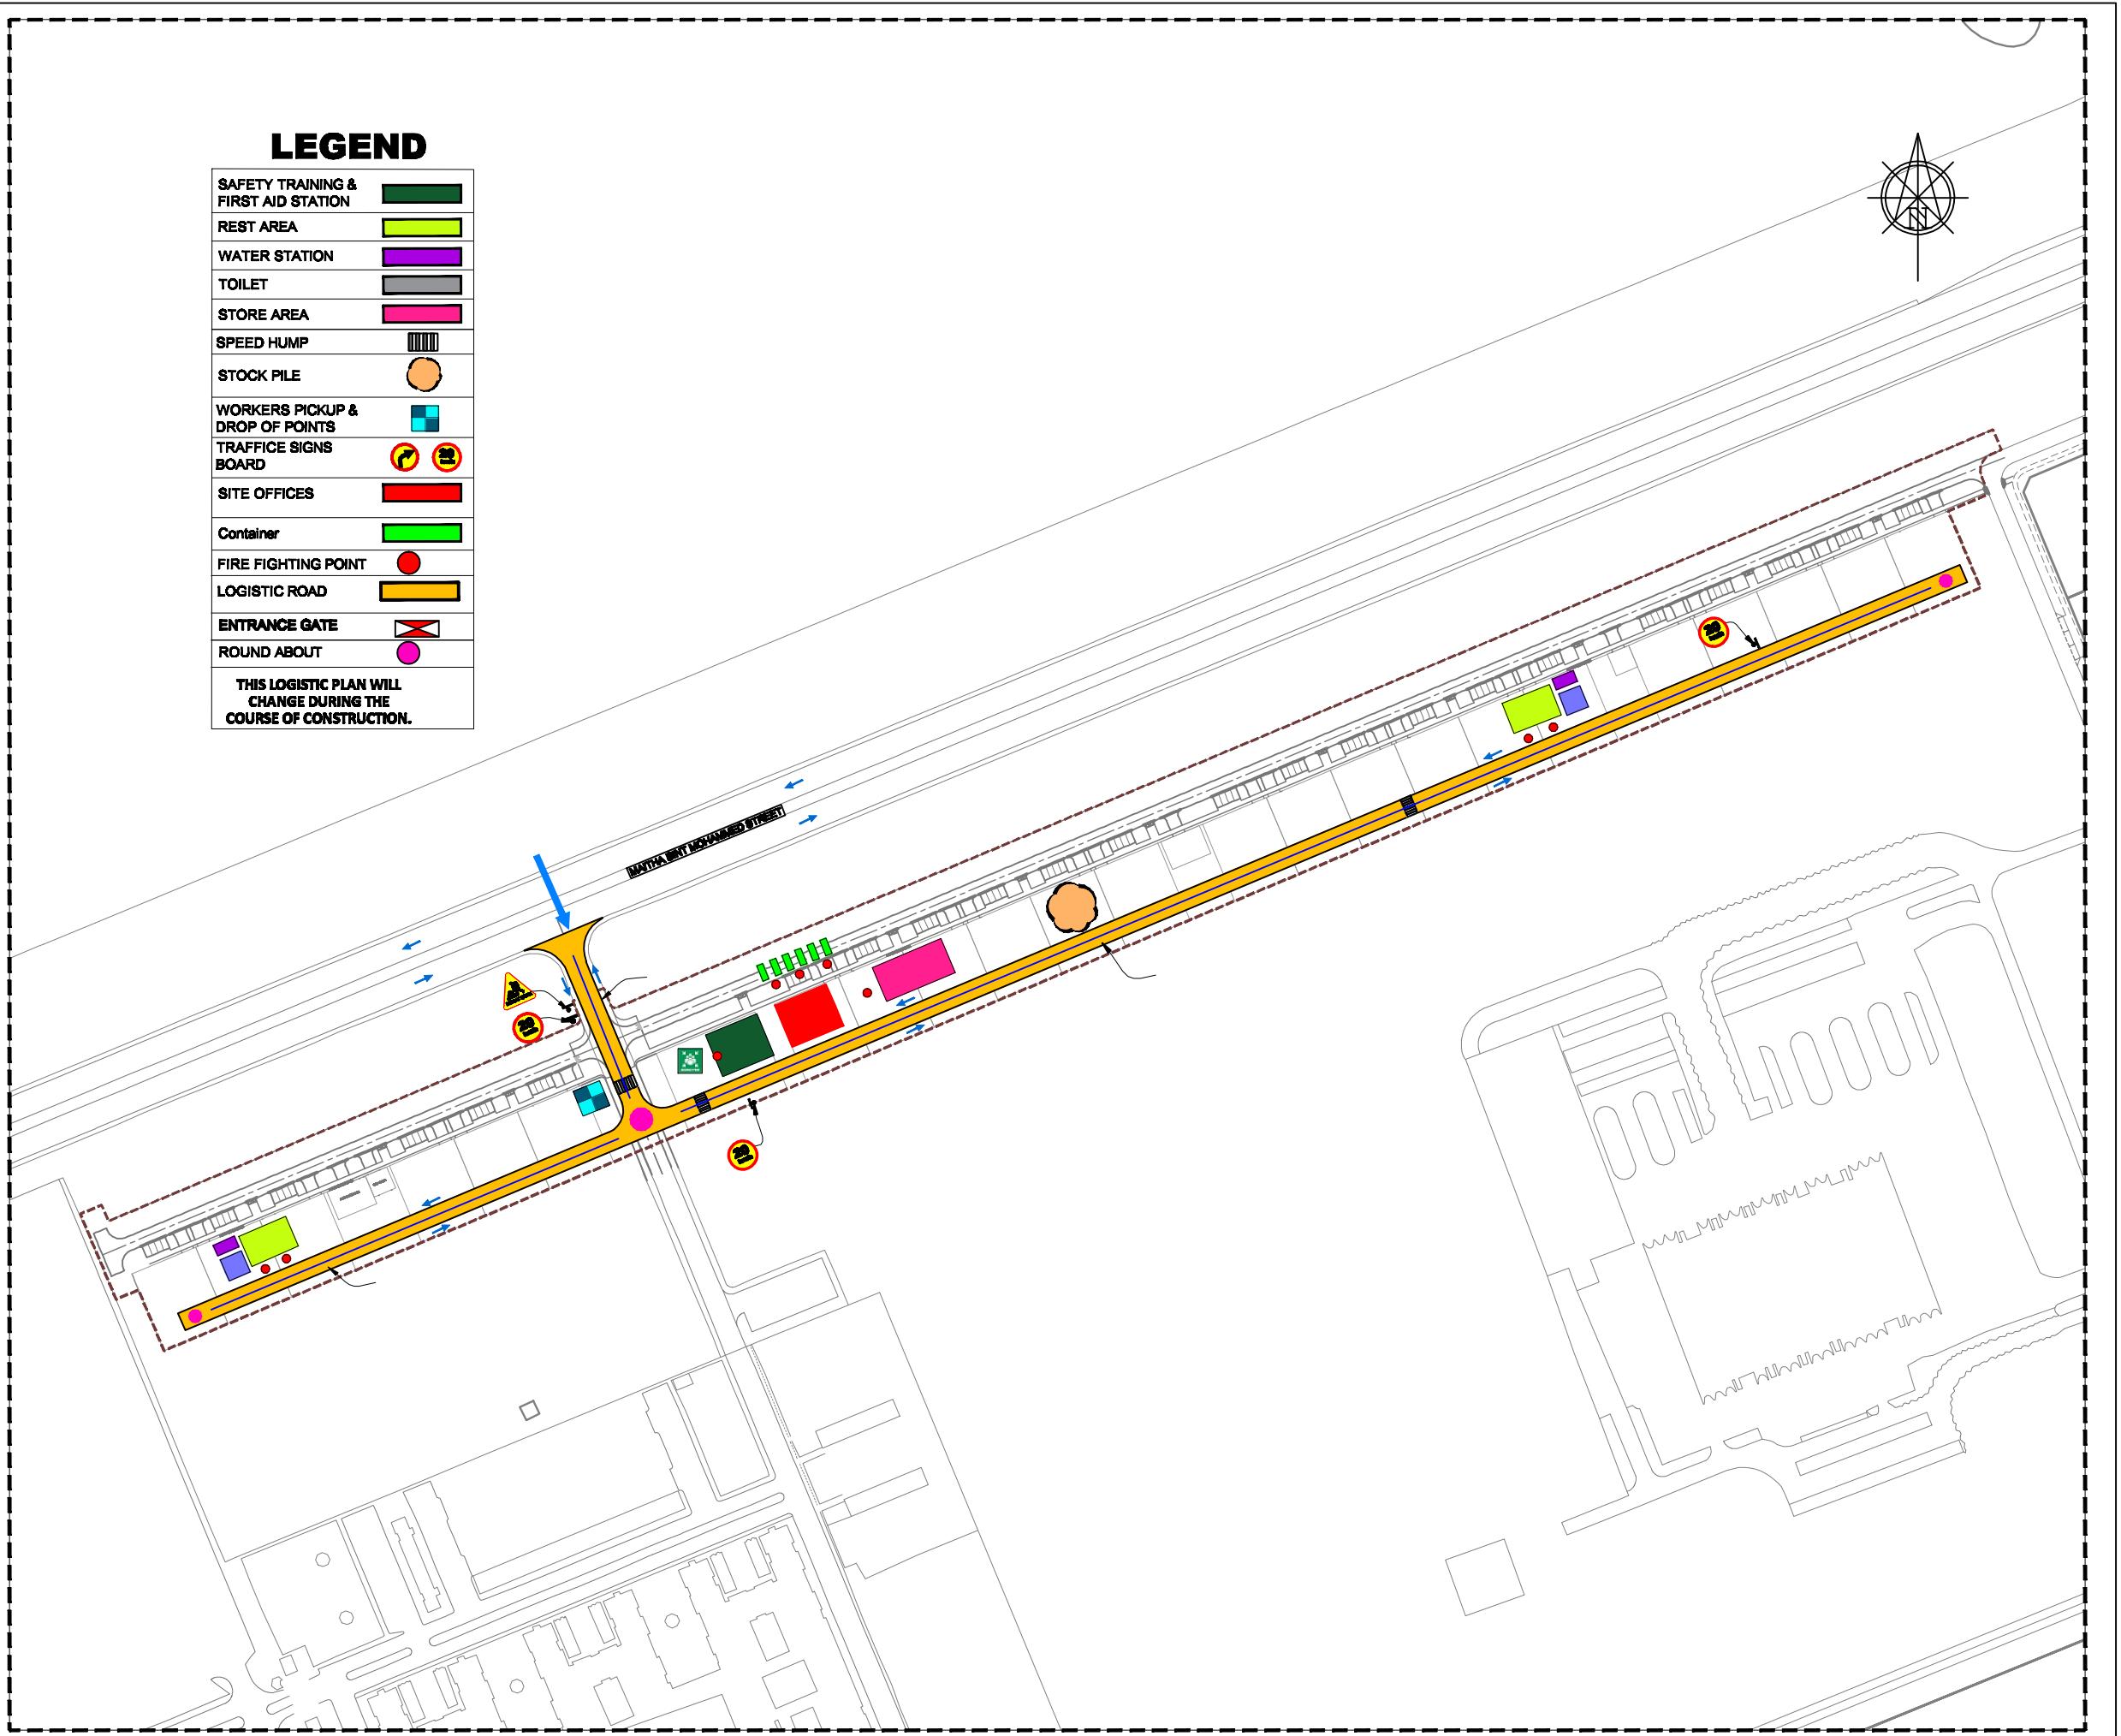

KEY PLAN

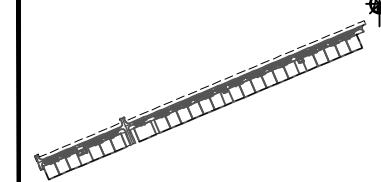

MOTR

1. COORDINATE SYSTEM IS BASED ON WGS84-UTM ZONE 40.
 2. ALL DIAMETERS AND COORDINATES ARE IN METER.

LXVII

ASSEMBLY POINT	
SAFETY TRAINING & FIRST AID STATION	
REST AREA	
WATER STATION	
TOILET	
STORE AREA	
SPEED HUMP	
STOCK PILE	
WORKERS PICKUP & DROP OF POINTS	
TRAFFICE SIGNS BOARD	
SITE OFFICES	
Container	
FIRE FIGHTING POINT	
LOGISTIC ROAD	
ENTRANCE GATE	
ROUND ABOUT	
THIS LOGISTIC PLAN WILL CHANGE DURING THE COURSE OF CONSTRUCTION.	

2020 American Society of Clinical Oncology Annual Meeting | ASCO.org/2020

PROJECTILE STAGE - 2B INTERNAL ROADS IN
VARIOUS AREAS IN AL AIN
AL AQABYYAH SITE

LOGISTIC LAYOUT PLAN (AL AQABIYYAH)

DESIGN	DRAWN	CHECKED	APPROVED
-----	M.J.A.	B.R.G.M.L.	B.R.G.M.L.
SCALE = N.I.S @ A1	ORIGINAL SIZE = A1	DATE	28/04/20
REF ID: DWG/001			
Sheet No : 1/084	Version Number : RAS GHUMAT		
Projection : UTM	Date	Time : 4PM	
DRAWING STATE		REV C	
SHOP DRAWING			
DRAWING NO. 828R-IN-NBH-AQ-ZZ-XX-AD-LO-0000			